

K A T A S T E R N A C H W E I S					
Berlin, Verwaltungsbezirk : Tempelhof					
Gemarkung Mariendorf Flur : 40120					
Flurstück	Fläche	Lg. B. Nr.	Grundbuch		Eigentümer
			Band	Blatt	
5/366	784 qm	4058	141	5081	Breschling, Kurt, Kaufm. Ange- stellter und Ehefrau Julia geb. Naumann, Lehrerin

LAGEPLAN Berlin - Mariendorf Furkastraße 88a

Die Anfertigung nach amtlichen Urbemessungen und die Richtigkeit des Planes
bescheinigt:


1. r d. Bezugsbezeichnung Nr. 76 v. 1969
w. z. i. s. e. m. Tempelhof von Berlin
Abt. Bau- und Wohnungswesen
Berlin 75 (Lichterfelde), den 5. April 1968
Hilfsweghauer Straße 204, Telefon 737873
Projektführer vom 26. 9. 1968

Grenzbeseinigung ist nicht erforderlich!
F L A C H E N N A C H W E I S
Grundstückgröße n. d. Kataster
abzüglich Vorgarten 3,00 x 4,00
abzüglich abzufr. Straßenland
Baugrundstück
bebaubar in Bauz. 11/2

784,00 qm	=	784,00 qm
-12,00 qm	=	-12,00 qm
-12,00 qm	=	-12,00 qm
760,00 qm	=	760,00 qm
152,00 qm bzw.	=	304,00 qm

proj. Bebauung Wohnhaus, 1 Gesch. 10,332 x 12,592	=	130,10 qm x 1 G.	=	130,10 qm
gesamte Bebauung noch bebaubar	=	130,10 qm	=	130,10 qm
Geschoßflächenzahl	=	21,90 qm	=	21,90 qm
	=	0,17	=	0,17
	=	130,10	=	130,10
	=	760,00	=	760,00

Geprüft
Berlin Tempelhof, den 4. 11. 1968
Bezirksamt Tempelhof von Berlin
Abt. Bau- u. Wohnungswesen
Bauaufsichtsrat
Steuere

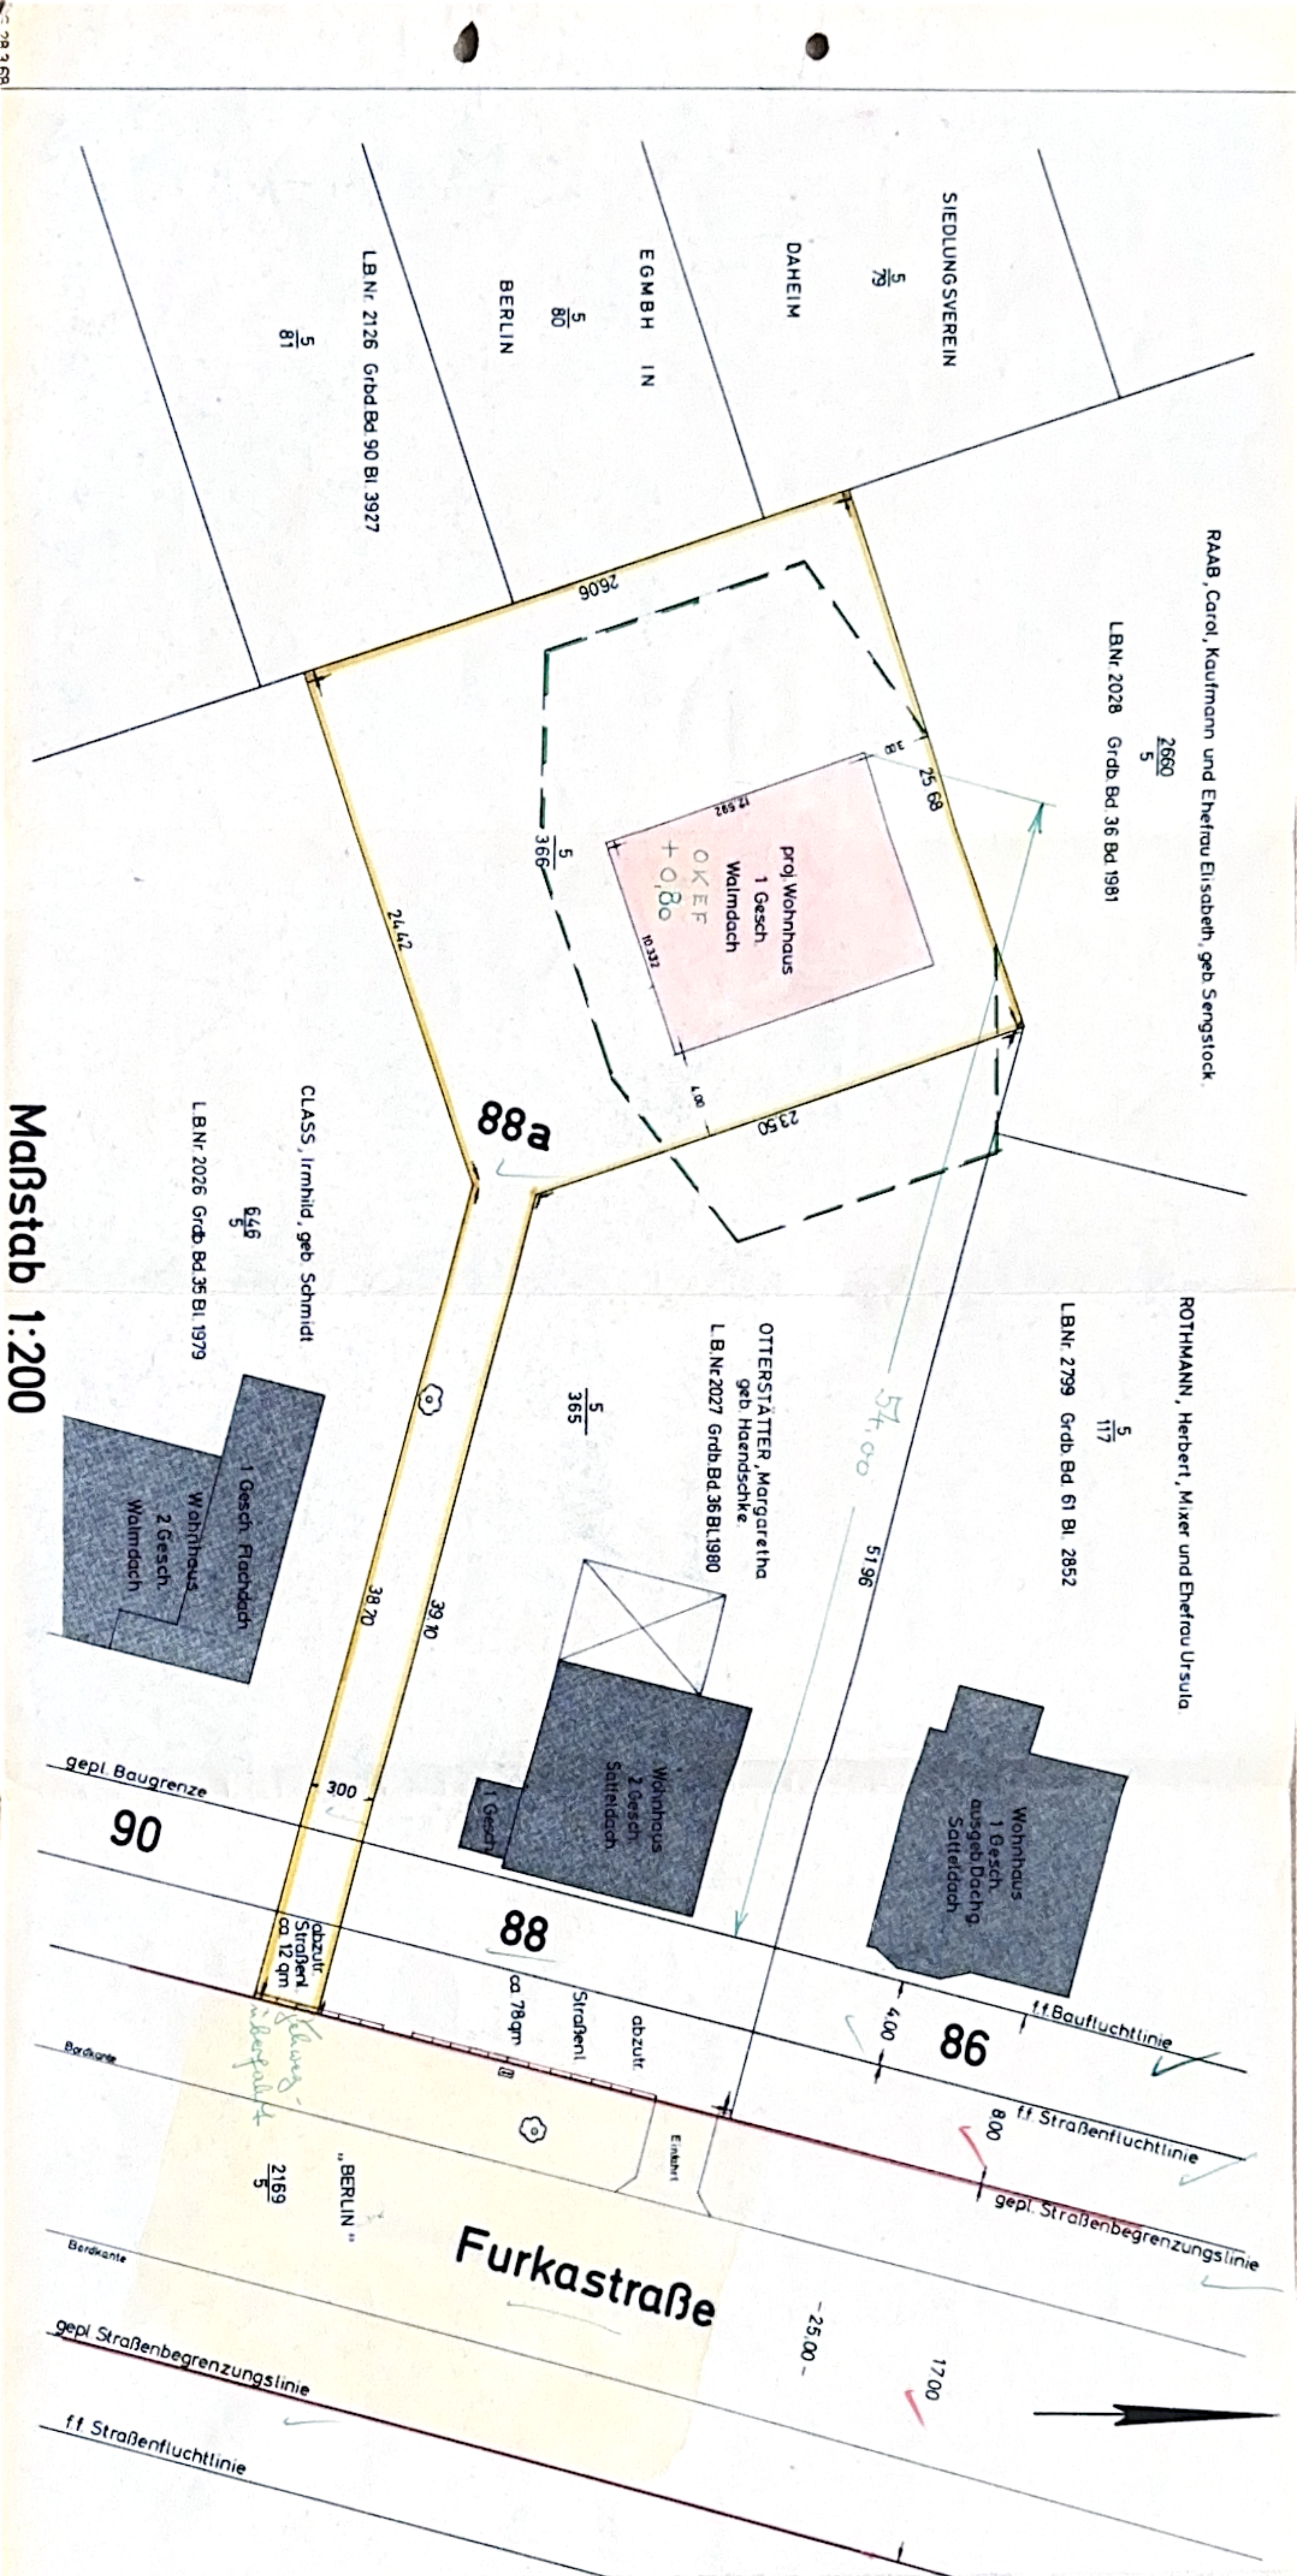

Maßstab 1:200